Suíte 01 — Planta arquitetônica v1 (sem mobiliário)

Geometria atualizada com o levantamento de 30/10/2026 · medidas em metros · pé-direito 2,64 m

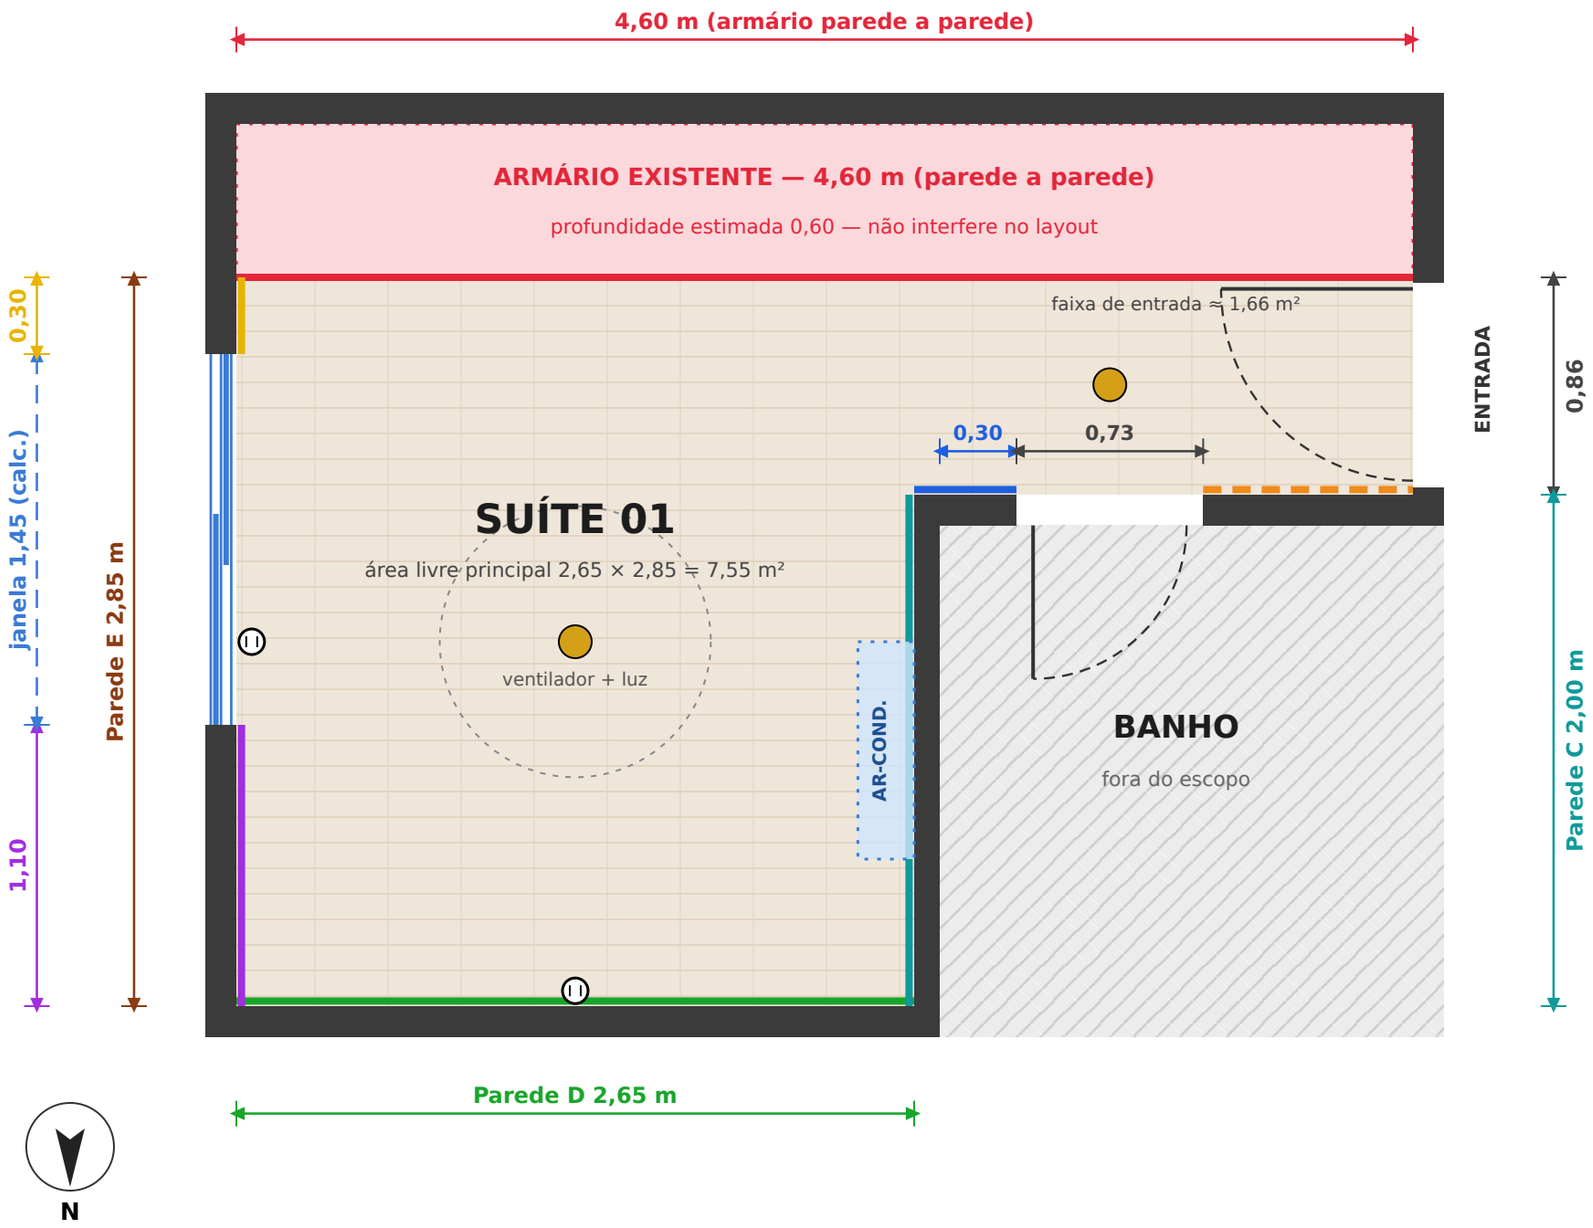

LEGENDA

- Confirmada
- Calculada
- Estimada
- Parede (espessura estimada 12 cm)
- Ar-condicionado existente (larg. est.)
- Ponto de luz existente
- ○ ‖ Tomada existente (meio da Parede D e E)

DADOS DO LEVANTAMENTO

Pé-direito: 2,64 m (conf.)
Janela: correr, 2 folhas · peitoril 1,00 m
altura 1,20 m · largura 1,45 m (calc.)
persiana de enrolar metálica externa
Porta de entrada: 0,80 c/ batente · folha 0,75
Porta do banheiro: 0,73 c/ batente · folha 0,60
Norte: a Parede D está voltada ao norte
→ a janela da Parede E fica a LESTE (sol da manhã)
Piso: madeira colante nova (fora do orçamento)

PENDÊNCIAS / INCONSISTÊNCIAS

⚠ **2,65 + parede + 0,30 + 0,73 + 1,10 = 4,78 + parede** ultrapassa os 4,60 m. O trecho 1,10 foi desenhado até 4,60. Não afeta a área mobiliável.

⚠ **Espessura das paredes: estimada**

⚠ **Sentido de abertura da porta de entrada: estimado**

⚠ **Largura do ar-condicionado: estimada (0,85)**

Parede E 2,85 × (2,00 + 0,86 = 2,86): 1 cm de diferença, dentro da tolerância

escala gráfica (1 m = 140 px)

0 0,5 1 m